


FILE NAME: \\njdot\proj\6700_NJ\DOT_R\6700_CADD\Plan_Sett\6700\00-Key.dgn
PEN TABLE: \\njdot\proj\6700_NJ\DOT_R\6700_CADD\Plan_Sett\6700\00-Key.dgn
REV DATE: 8/16/2024
SCALE: 2000.000000 1/in.

UTILITIES	
ATLANTIC CITY ELECTRIC	
SOUTH JERSEY GAS	
CITY OF MILLVILLE WATER AND SEWER	
VERIZON NJ	


DESIGN TRAFFIC DATA - RTE. 49		
A.D.T. (2013) - 2 WAY	=	21,935 VPD
A.D.T. (2015) - 2 WAY	=	22,435 VPD
A.D.T. (2025) - 2 WAY	=	23,740 VPD
A.D.T. (2035) - 2 WAY	=	25,115 VPD
D.H.V. (2015) - 2 WAY	=	1,955 VPH
D.H.V. (2025) - 2 WAY	=	2,070 VPH
D.H.V. (2035) - 2 WAY	=	2,190 VPH
D	=	54%
T	=	4%
V	=	30 M.P.H. (M.P. 36.23)

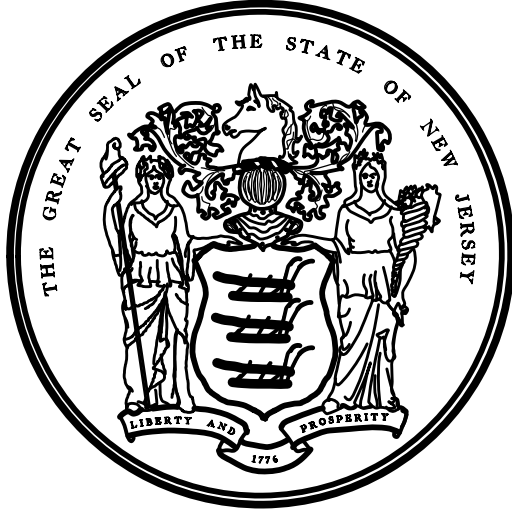

State of New Jersey
Department of Transportation
PLANS OF

ROUTE 49, BRIDGE OVER MAURICE RIVER
SUPERSTRUCTURE REPLACEMENT

CONTRACT NO. 036153140

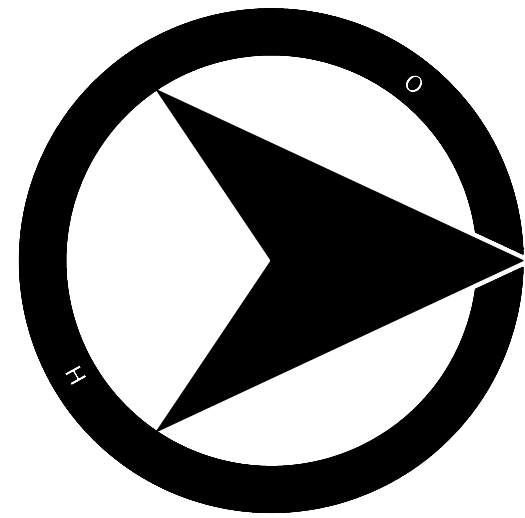


STATE	FEDERAL PROJECT NO.
N.J.	0049314

INDEX OF SHEETS	
SHEET NO.	DESCRIPTION
1	KEY
2-3	ESTIMATE-DISTRIBUTION OF QUANTITIES - ROADWAY
4-5	TYPICAL SECTIONS
6	PLAN SHEET INDEX
7	CONSTRUCTION LEGEND
8-9	CONSTRUCTION PLANS
10-13	ENVIRONMENTAL & SOIL EROSION & SEDIMENT CONTROL PLANS
14-17	DRAINAGE AND UTILITY PLANS
18-19	CURB RAMP LAYOUT DETAILS
20-38	CONSTRUCTION DETAILS
39	PROFILES
40-42	TIES
43	GRADES
44-59	TRAFFIC CONTROL (AND STAGING PLANS)
60	TRAFFIC SIGNAL PLANS
61-63	ELECTRICAL PLANS
64	TRAFFIC SIGNING AND STRIPING PLANS
65-69	CROSS SECTIONS
70	ESTIMATE OF QUANTITIES - BRIDGE
71-129	BRIDGE PLANS
VERIZON TELEPHONE CONDUIT SUPPORT PLANS	


STRUCTURES IN PROJECT LIMITS	
	DESCRIPTION
1	STRUCTURE NO. 0605-151: ROUTE 49 OVER MAURICE RIVER

MID-POINT OF PROJECT
LONGITUDE: 75°02'25"W
LATITUDE: 39°23'43"N

STANDARD ROADWAY
CONSTRUCTION/TRAFFIC
CONTROL/BRIDGE CONSTRUCTION
DETAILS BOOKLET, 2016, AND
STANDARD ELECTRICAL DETAILS
BOOKLET, 2007, ARE APPLICABLE TO
THIS PROJECT EXCEPT FOR THOSE
DETAILS CONTAINED HEREIN.

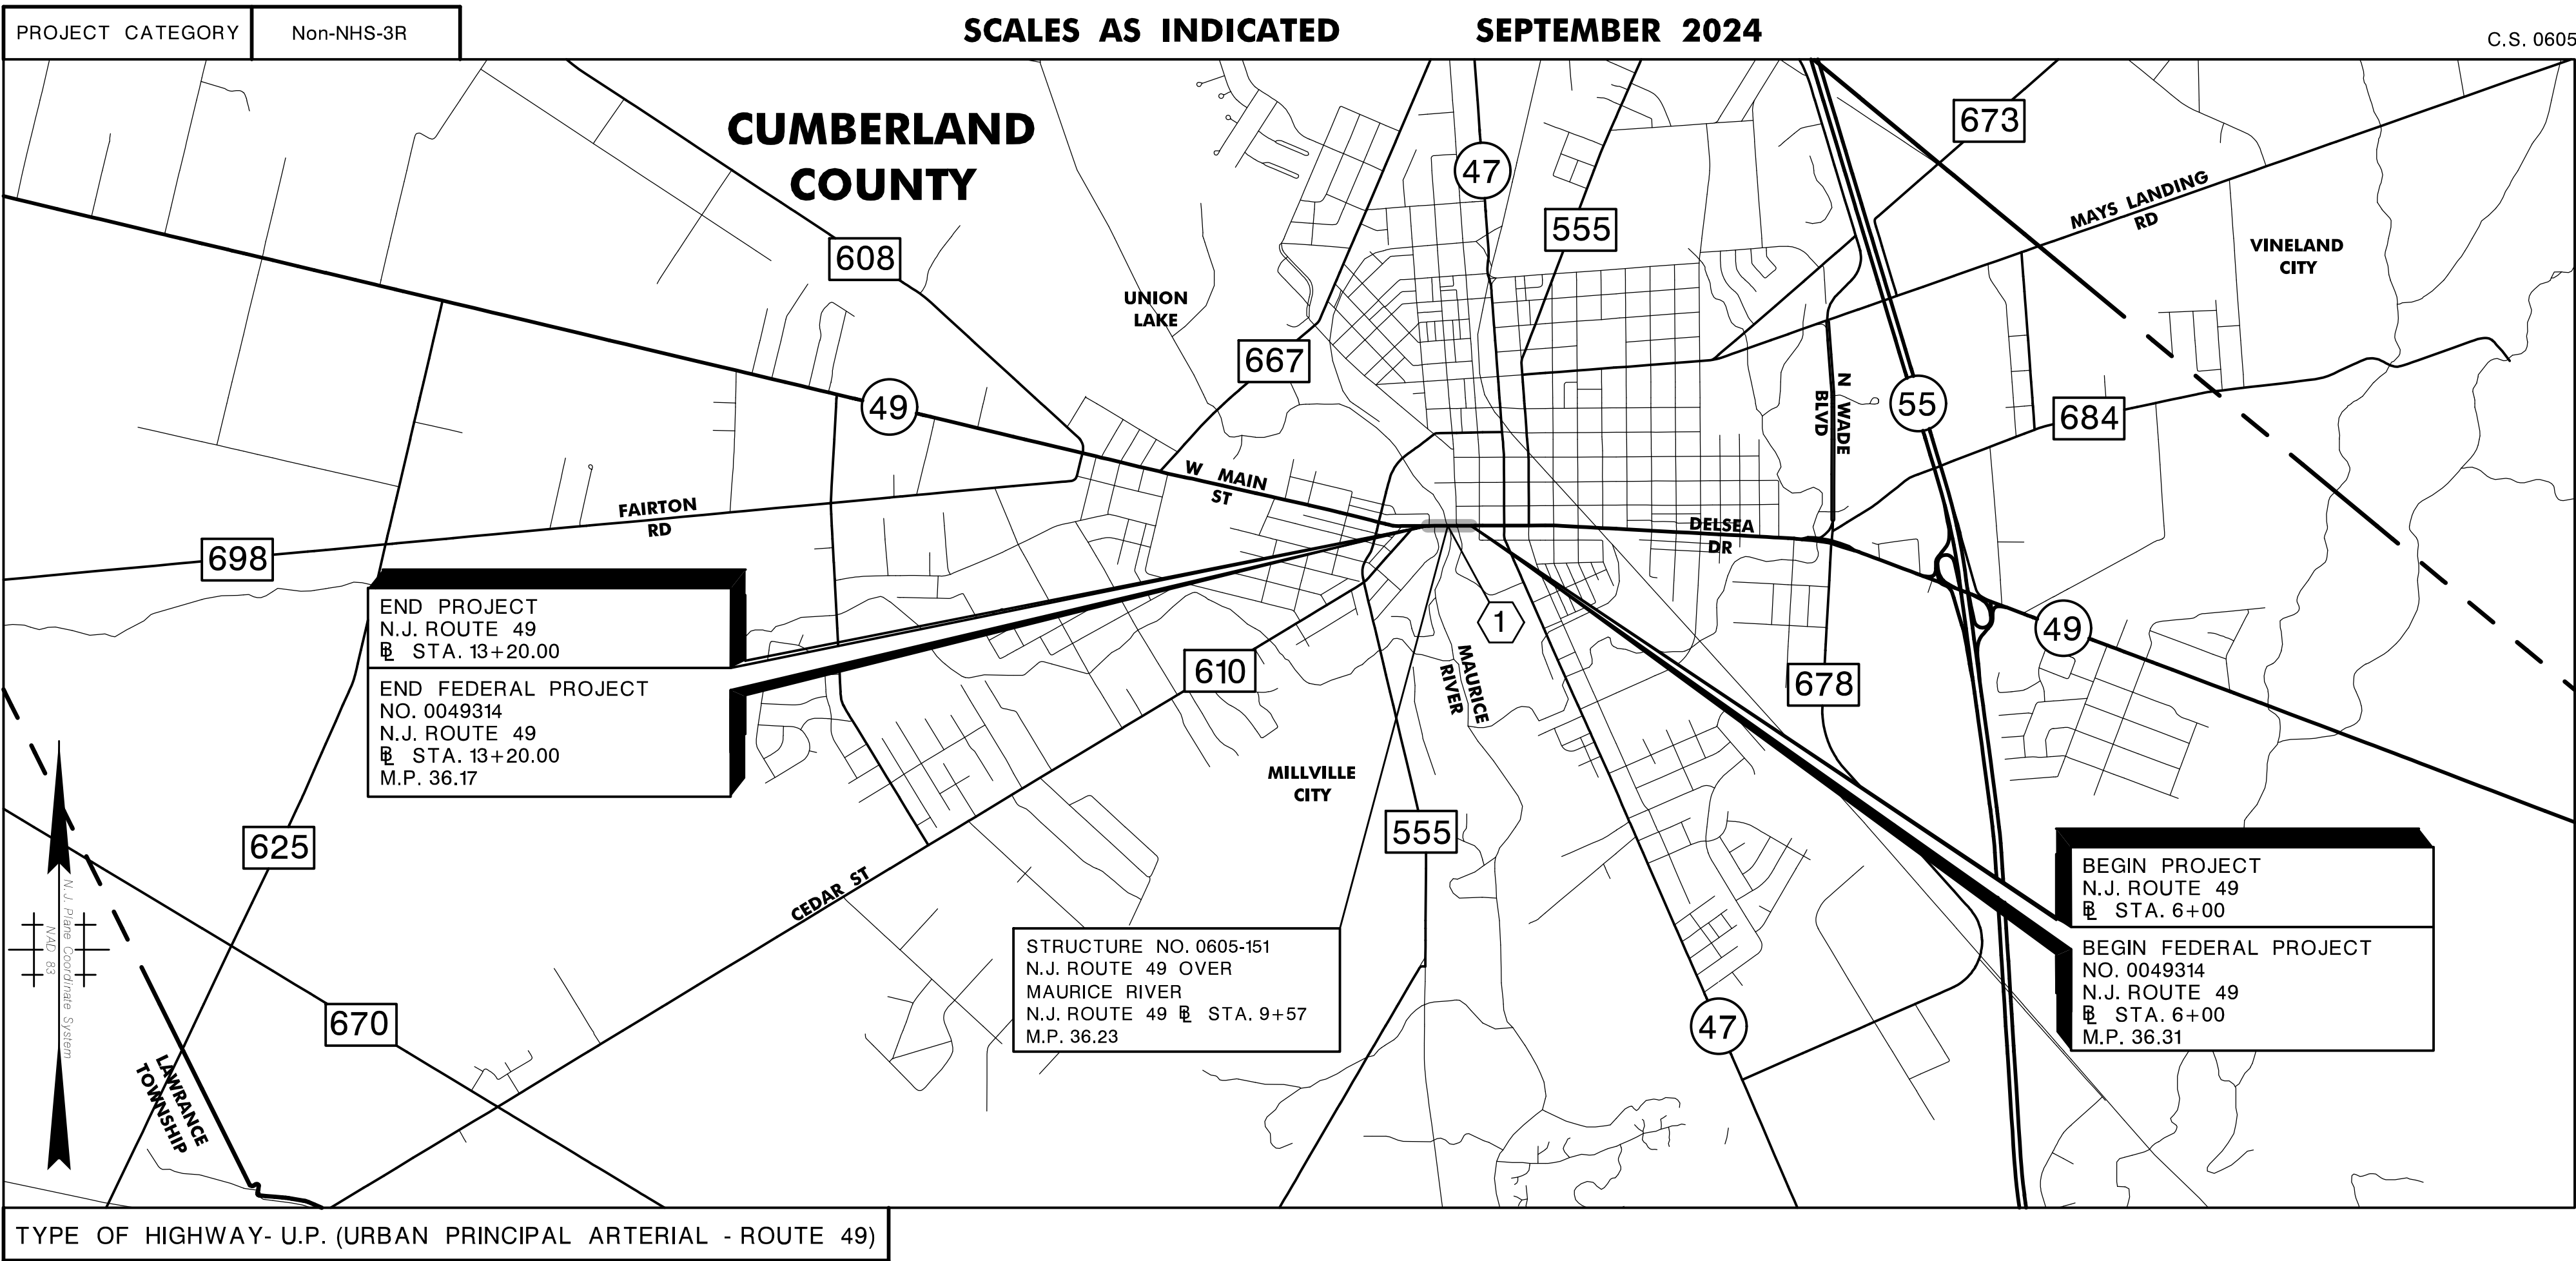

KEY MAP

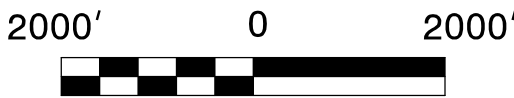

"CHANGES MADE TO THESE PLANS SINCE SIGNATURE BY THE CONSULTANT MAY BE DETERMINED BY COMPARISON OF THE PLANS FILED AT THE DEPARTMENT WITH THOSE FILES AT THE OFFICE OF THE CONSULTANT"



CERTIFICATION OF AUTHORIZATION NO. 24GA28044300	
	DATE: 8/16/2024
NABIL M. HOURANI, P.E.	
NEW JERSEY PROFESSIONAL ENGINEER LICENSE NO. 24GE03888900	

TOTAL LENGTH OF PROJECT= 720.00 LIN. FT. OR 0.14 MILES

TOTAL LENGTH OF FEDERAL PROJECT NO. 0049314 = 720.00 LIN. FT. OR 0.14 MILES

2019 STANDARD SPECIFICATIONS FOR ROAD AND BRIDGE CONSTRUCTION TO GOVERN

Submitted by		8/23/24
	Director, Division of Project Management	Date
Approved by		8/26/2024
	State Transportation Engineer	Date